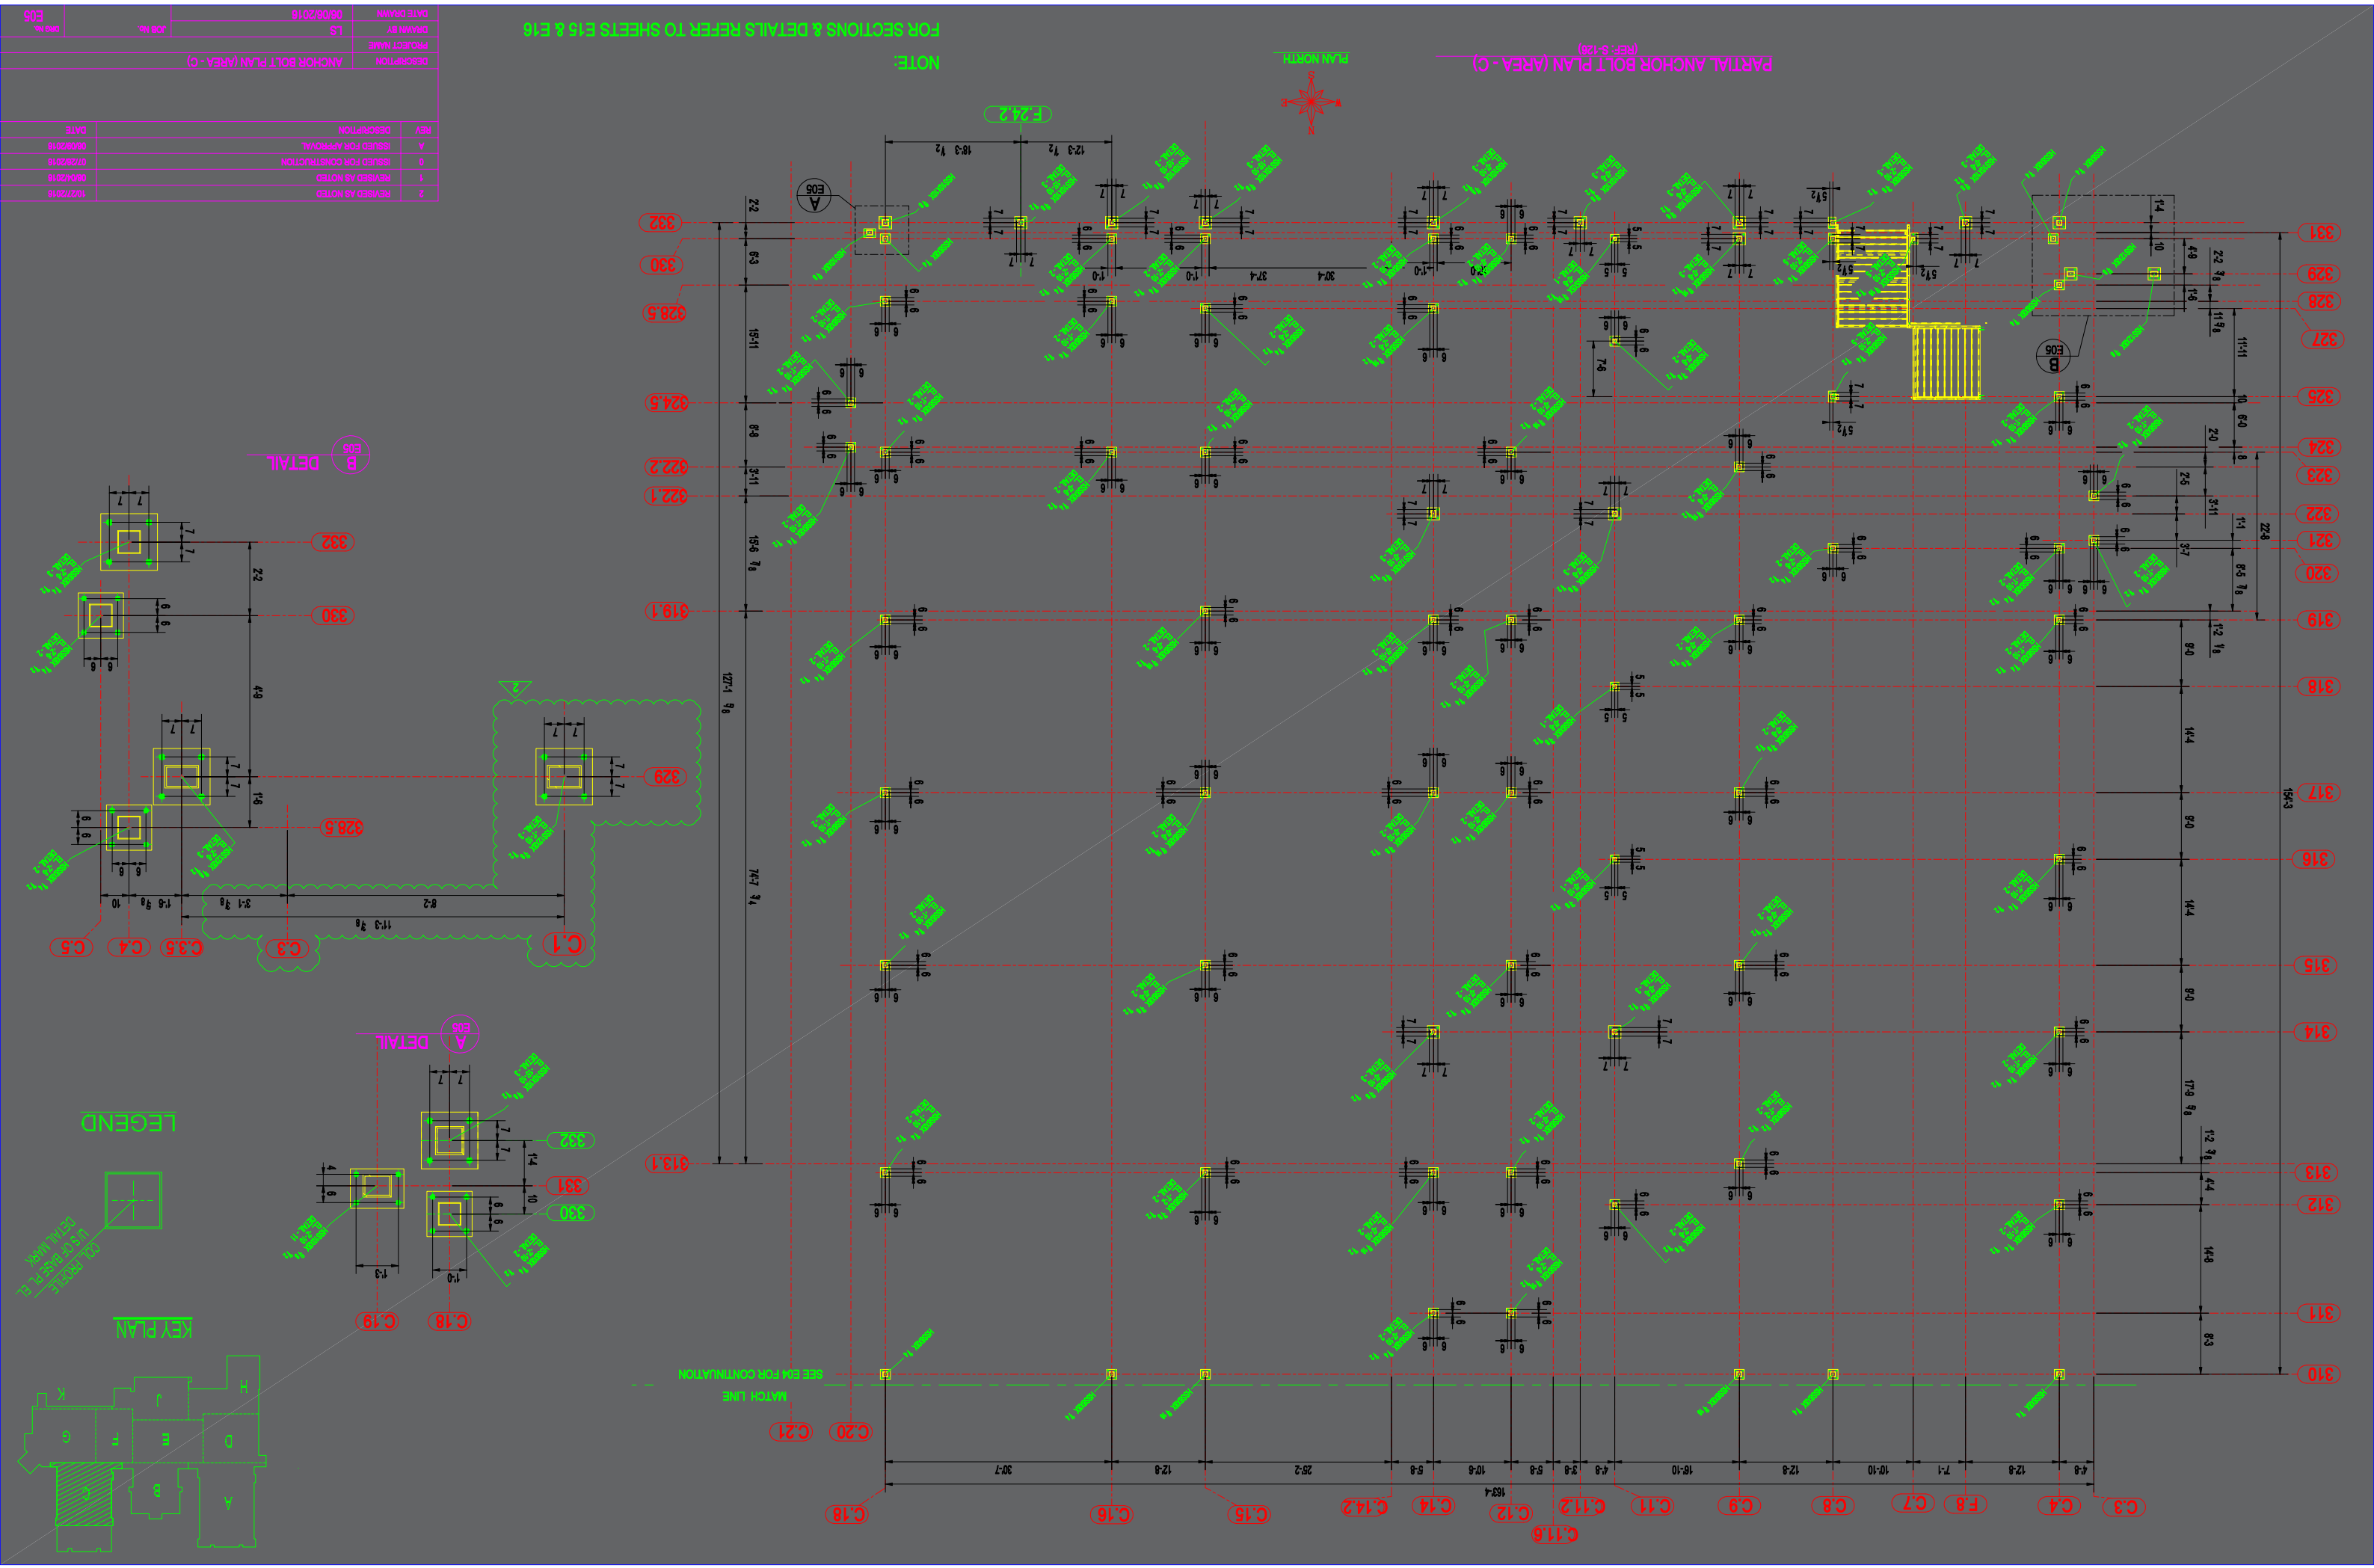

REV	DESCRIPTION	DATE
2	REVISED AS NOTED	10/27/2016
1	REVISED AS NOTED	08/24/2016
0	ISSUED FOR CONSTRUCTION	07/28/2016
A	ISSUED FOR APPROVAL	06/08/2016

DESCRIPTION	ANCHOR BOLT PLAN (AREA - C)
DRAWN BY	LS
PROJECT NAME	
DATE DRAWN	08/08/2016

JOB No.

DWG No. E05