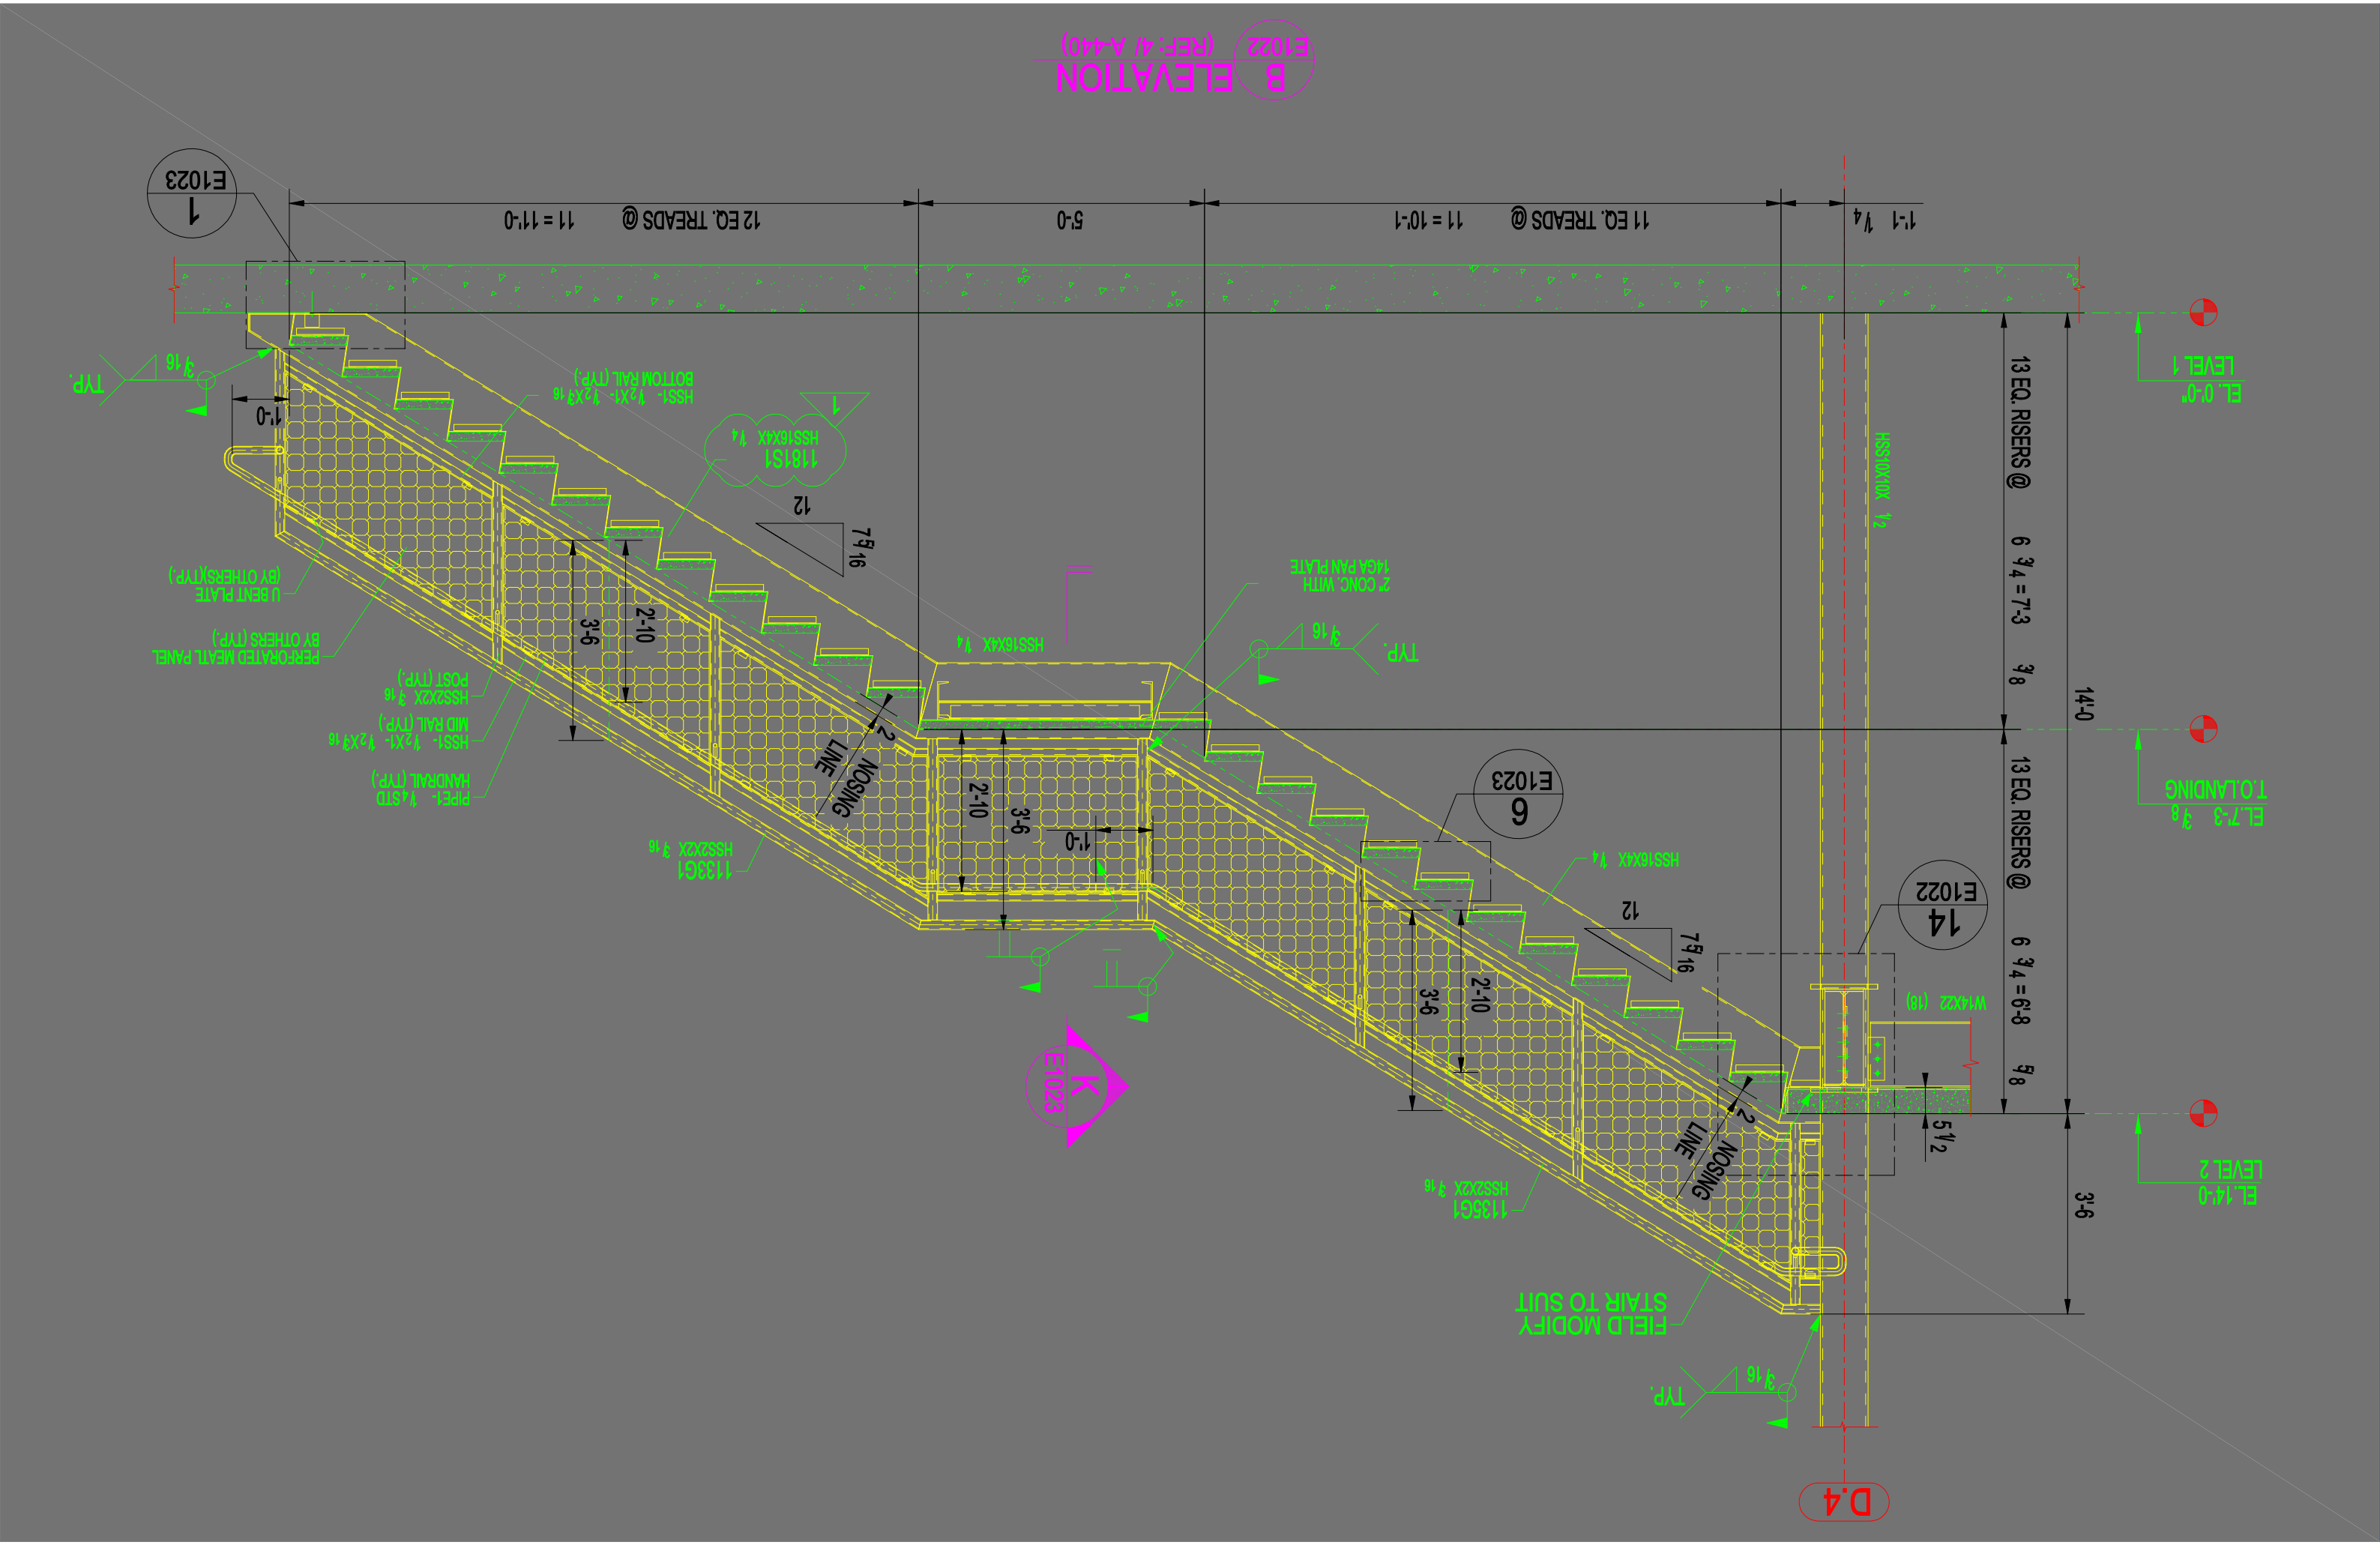
B ELEVATION
E1022 (REF: 4/ A-440)
EL. 0'-0"
LEVEL 1
EL. 14'-0
LEVEL 2
EL 7-3 3/8
T.O.LANDING
13 EQ. RISERS @ 6 3/4 = 7'-3 3/8
13 EQ. RISERS @ 6 3/4 = 6'-8 5/8
14'-0
3'-6
5 1/2
W14X22 (18)
HSS18X8X1/2
14
E1022
6
E1023
K
E1023
1
E1023
11 EQ. TREADS @ 11 = 10'-1
12 EQ. TREADS @ 11 = 11'-0
1'-1 1/4
5'-0
12
7 9/16
2'-10
3'-6
1'-0
NOSING LINE
HSS18X4X1/4
TYP.
3/16
FIELD MODIFY STAIR TO SUIT
2" CONC. WITH MGA PAN PLATE
HSS18X4X1/4
HSS6X6X3/16
PERFORATED METAL PANEL BY OTHERS (TYP.)
U BENT PLATE (BY OTHERS TYP.)
HSS6X6X3/16 POST (TYP)
HSS6X6X3/16 MID RAIL (TYP.)
PIPE1-1/2STD HANDRAIL (TYP)
HSS1-1/2X1-1/2X3/16 BOTTOM RAIL (TYP.)
HSS18X4X1/4
11331
HSS6X6X3/16
11330
HSS6X6X3/16
D.4