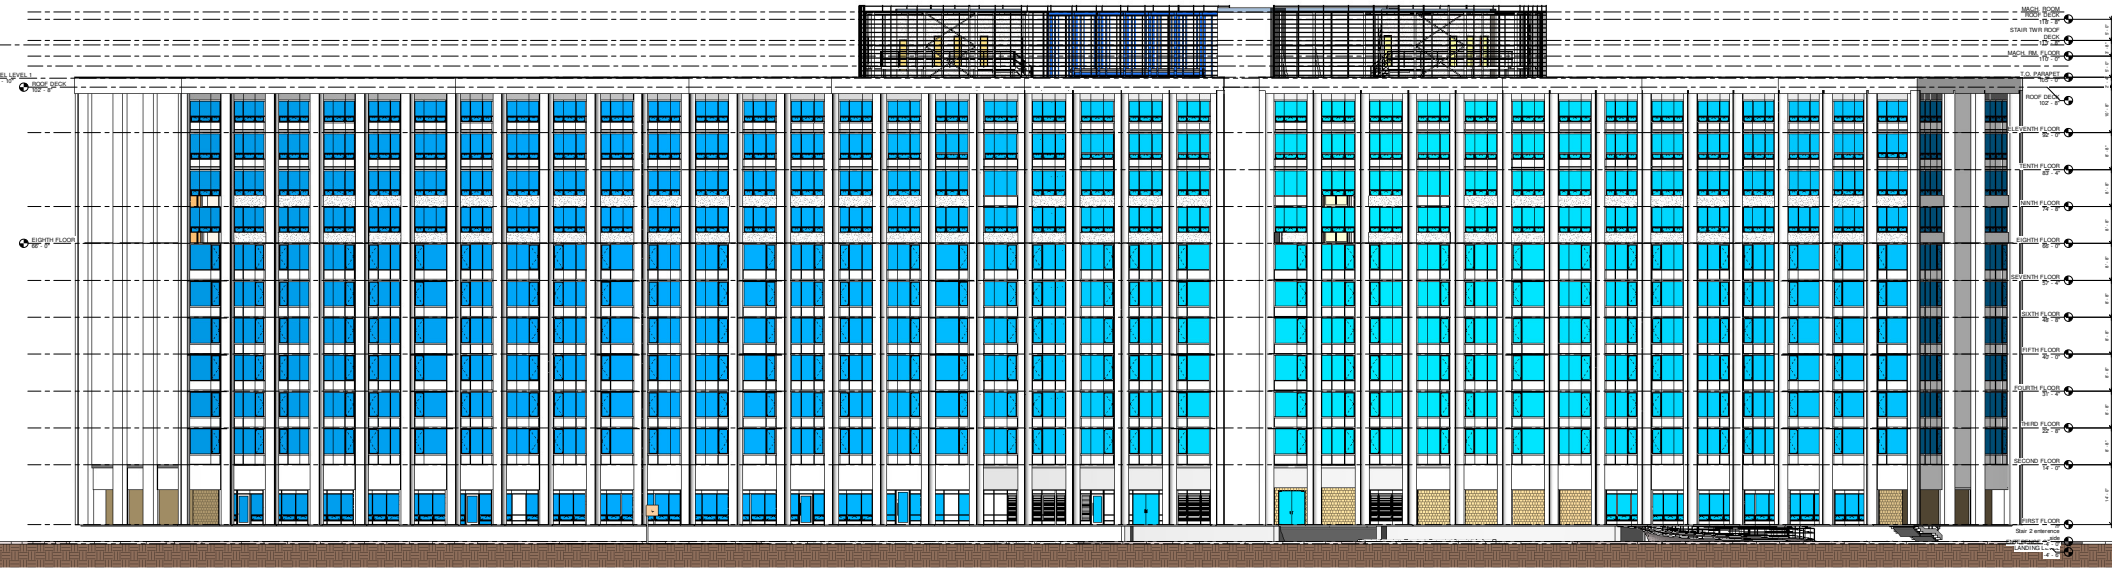
MACH. ROOM
ROOF DECK
113 - 3"
STAIR TWR ROOF
DECK
113 - 3"
MACH. RM. FLOOR
110 - 3"
T.O. PARAPET
106 - 6"
ROOF DECK
102 - 6"
ELEVENTH FLOOR
95 - 10"
TENTH FLOOR
87 - 2"
NINTH FLOOR
78 - 6"
EIGHTH FLOOR
69 - 10"
SEVENTH FLOOR
61 - 2"
SIXTH FLOOR
52 - 6"
FIFTH FLOOR
43 - 10"
FOURTH FLOOR
35 - 2"
THIRD FLOOR
26 - 6"
SECOND FLOOR
18 - 10"
FIRST FLOOR
Stair 2 entrance
SIDEWALK
LANDING LEVEL
ROOF DECK
102 - 6"
EIGHTH FLOOR
69 - 10"
EL LEVEL 1
0" - 0"