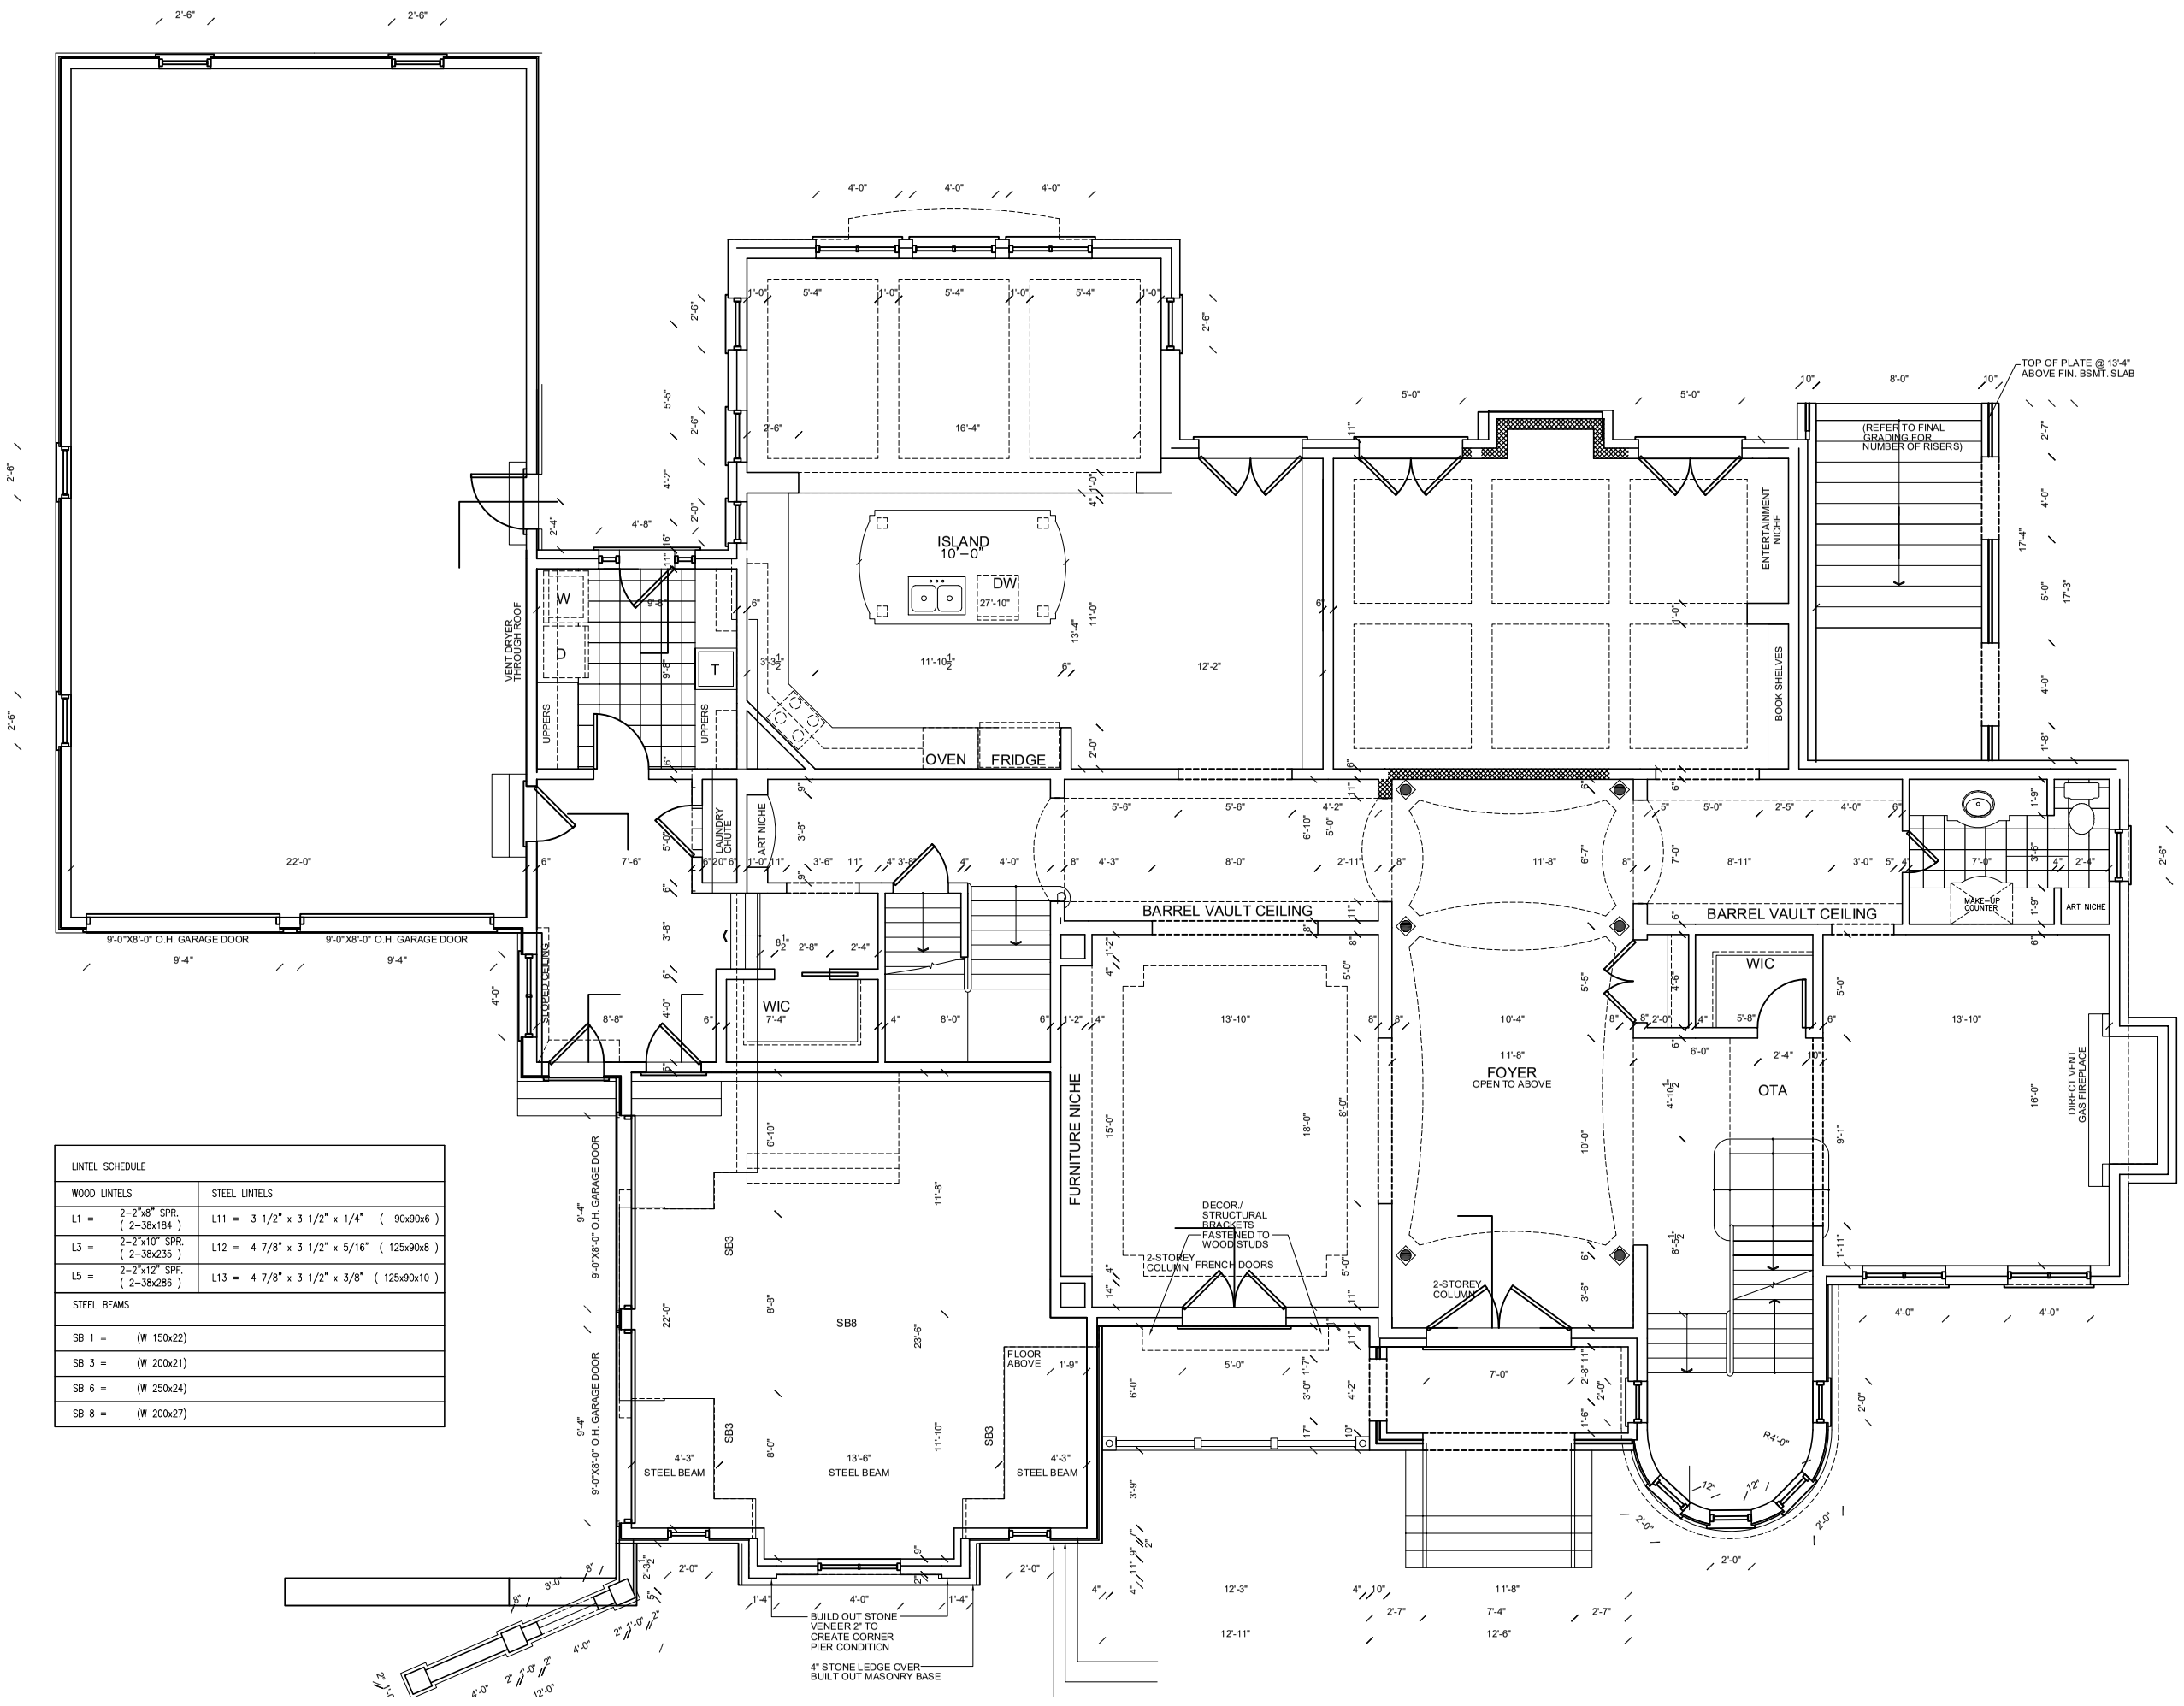

LINTEL SCHEDULE	
WOOD LINTELS	STEEL LINTELS
L1 = 2-2"x8" SPR. (2-38x184)	L11 = 3 1/2" x 3 1/2" x 1/4" (90x90x6)
L3 = 2-2"x10" SPR. (2-38x235)	L12 = 4 7/8" x 3 1/2" x 5/16" (125x90x8)
L5 = 2-2"x12" SPF. (2-38x286)	L13 = 4 7/8" x 3 1/2" x 3/8" (125x90x10)
STEEL BEAMS	
SB 1 = (W 150x22)	
SB 3 = (W 200x21)	
SB 6 = (W 250x24)	
SB 8 = (W 200x27)	

JOB N?.
QUBTI RESIDENCE
0601

DWN BY:
OQ

SCALE:
1/8" = 1'-0"

DATE ISSUED:

PROJECT
VAUGHAN
ONTARIO

CLIENT
RAMZI QUBTI

S.F.
(INCL. 148 S.F. O.T.B.)

UNIT

PAGE NO.