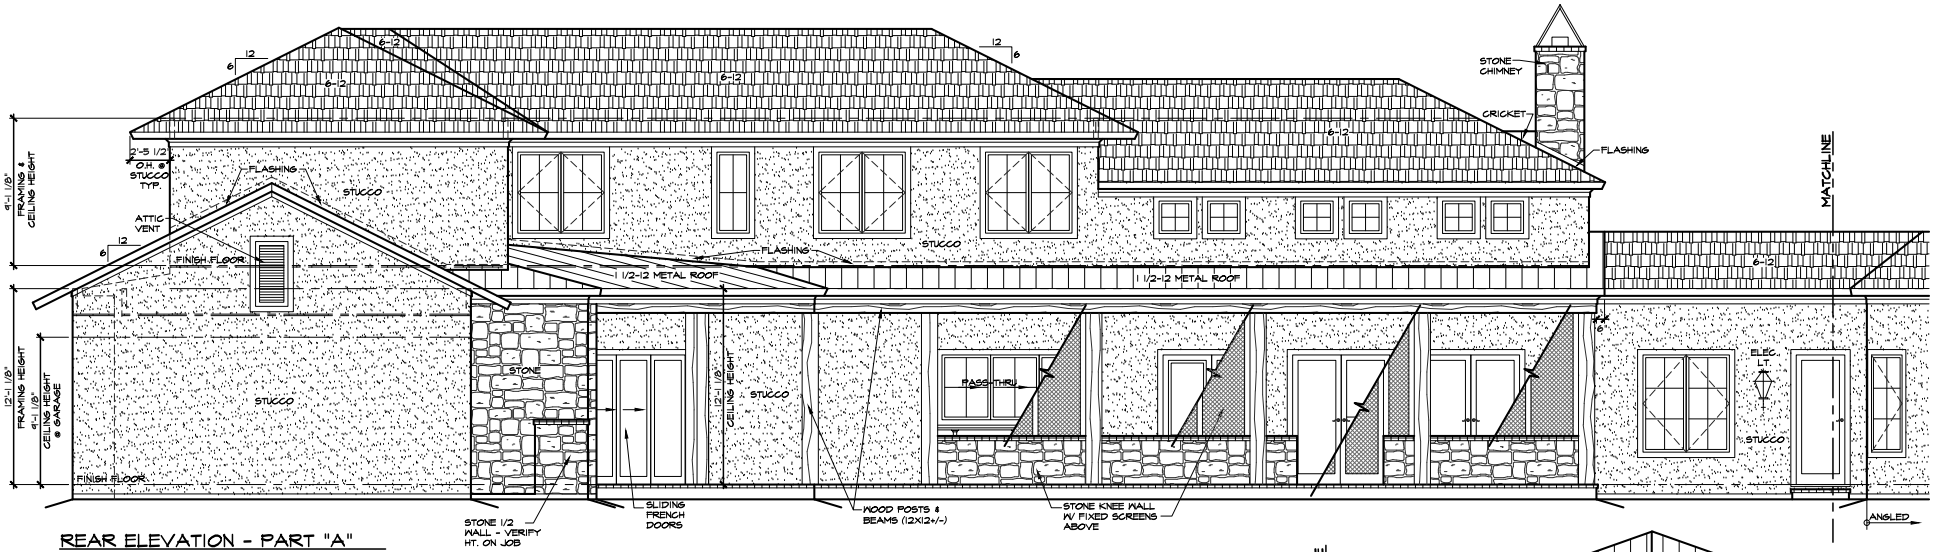

REAR ELEVATION - PART "A"

SCALE: 1/4"=1'-0"

ELEVATION GENERAL NOTES:

- ALL FIRST FLOOR CEILING HEIGHTS TO BE 12'-1 1/8" HIGH, UNLESS OTHERWISE NOTED.
- ALL SECOND FLOOR CEILING HEIGHTS TO BE 9'-1 1/8" HIGH, UNLESS OTHERWISE NOTED.
- ALL EXTERIOR MATERIALS TO BE STONE, UNLESS OTHERWISE NOTED.
- ALL WINDOWS AT STONE TO HAVE 4" STUCCO TRIM AS SHOWN ON ELEVATIONS, UNLESS OTHERWISE NOTED.
- ALL HORIZONTAL STONE OPENINGS TO BE SUPPORTED BY 4" X 5" X 3/8" STEEL ANGLE, UNLESS OTHERWISE NOTED. VERIFY WITH ENGINEER.
- STONE SHELF TO FOLLOW FINISH GRADE, MIN. 5 1/2" WIDE.
- ALL DOOR AND WINDOW TRIM AT STUCCO TO BE 4" STUCCO, UNLESS OTHERWISE NOTED.
- ALL FLASHING, CRICKETS AND GABLE ROOF VENTS TO BE COPPER, UNLESS OTHERWISE NOTED (VERIFY W/ OWNER).
- ROUTE ALL STACKS AND VENTS TO BACKSIDE OF ROOF. ALL PLUMBING STACKS TO BE "RE-VENTED" WHERE POSSIBLE FOR MIN. # OF ROOF PENETRATIONS.

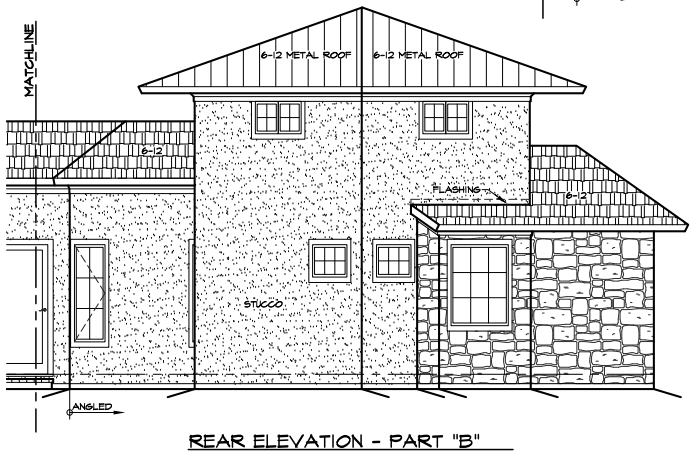

REAR ELEVATION - PART "B"

SCALE: 1/4"=1'-0"

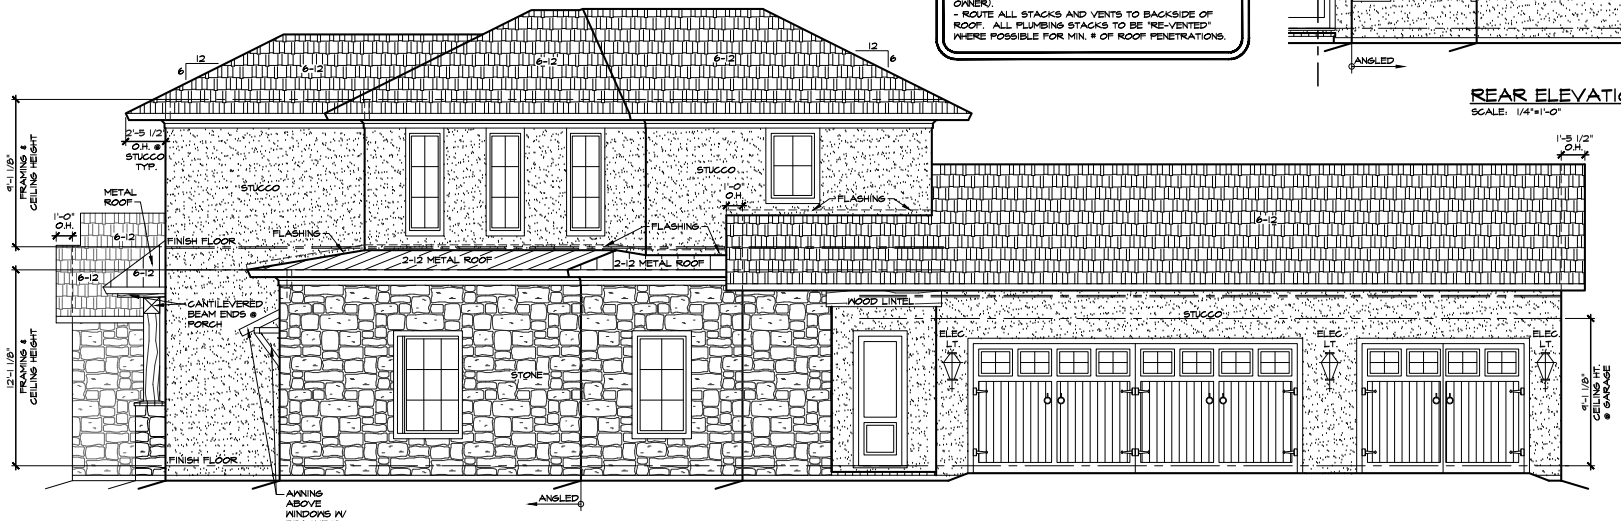

RIGHT ELEVATION

SCALE: 1/4"=1'-0"