ELECTRICAL SYMBOLS

- 110V DUPLEX WALL RECEPTACLE
- 42" 110V DUPLEX WALL RECEP. MTD. 42" AFF.
- 110V DUPLEX WALL RECEPTACLE - HIDDEN
- WP 110V WEATHER PROOF DUPLEX OUTLET
- GFI GROUND FAULT INTERRUPTER
- USB 110V DUPLEX WALL RECEPTACLE W/ USB CHARGING PORT
- 110V 4-PLEX OUTLET
- 110V DUPLEX FLOOR RECEPTACLE
- TELEPHONE FLOOR RECEPTACLE
- 220 220V WALL RECEPTACLE
- TELEPHONE OUTLET
- T.V. ANTENNA OUTLET
- WALL MOUNTED LIGHT FIXTURE
- CEILING MOUNTED LIGHT FIXTURE
- RECESSED FIXTURE
- RECESSED SOFFIT LIGHT
- RECESSED EYEBALL (E.B.) OR WALL WASHER (W/W)
- LV RECESSED LOW VOLTAGE FIXTURE
- SOFFIT MOUNTED FLOOD LIGHT
- CEILING FAN
- DOUBLE POLE SWITCH
- 3 TRIPLE POLE SWITCH
- A AIR SWITCH
- D DIMMER SWITCH
- DS DOOR SWITCH
- MS MOTION SENSOR SWITCH
- S STEREO SPEAKER - CEILING MOUNTED
- I INTERCOM- WALL MOUNTED
- SMOKE DETECTOR
- DOOR CHIMES
- PUSH BUTTON (PB) OR DOOR BELL (DB)
- 1X4 FLUORESCENT
- 2X4 FLUORESCENT
- UNDER CABINET LIGHTING
- F FUSED DISCONNECT - SIZE AS REQ'D.
- STAIR LTS. - RECESSED IN WALL
- ELECTRIC MOTOR (SEE NOTE ON PLAN)

NOTE:
-ELECTRICAL CONTRACTOR TO VERIFY PANEL SIZE AND LOCATION PRIOR TO CONSTRUCTION.
-VERIFY OUTLET HEIGHTS AT ALL CABINETRY WITH MILLWORK ELEVATIONS.
-VERIFY WIRING FOR APPLIANCES AND MECHANICAL SYSTEMS WITH MANUFACTURER SPECIFICATIONS.

A/C UNITS & WATER HEATERS

WATER HEATER #1 TANKLESS W/H TO SERVE: MASTER BATH	A/C UNIT #1 TO SERVE MASTER SUITE, BEDROOM #2 SUITE, & PLAYROOM - VER. SIZE W/ MECH. CONTRACTOR
WATER HEATER #2 TANKLESS W/H TO SERVE: BATH #2 & 1/2 BATH	A/C UNIT #2 TO SERVE: 1st FLOOR EXCEPT MASTER SUITE, BEDROOM #2 SUITE, & PLAYROOM - VER. SIZE W/ MECH. CONTRACTOR
WATER HEATER #3 TANKLESS W/H TO SERVE: 2nd FLOOR	A/C UNIT #3 TO SERVE: 2nd FLOOR - VER. SIZE W/ MECH. CONTRACTOR
WATER HEATER #4 TANKLESS W/H TO SERVE: KITCHEN, OUTDOOR KITCHEN, & BAR	

NOTE:
- ALL A/C UNITS AND W/H IN ATTIC TO BE LOCATED IN G.I. SAFETY PANS W/ DRAIN TO SOFFIT, UNLESS OTHERWISE NOTED.
- ALL A/C UNITS AND W/H IN ATTIC TO BE ACCESSIBLE BY A 24" WIDE PLYWOOD CATWALK. PROVIDE A 30" WIDE PLYWOOD PLATFORM AROUND ALL UNITS.
-VERIFY LOCATION & QUANTITY OF ALL W/H & A/C UNITS W/ BUILDER!!

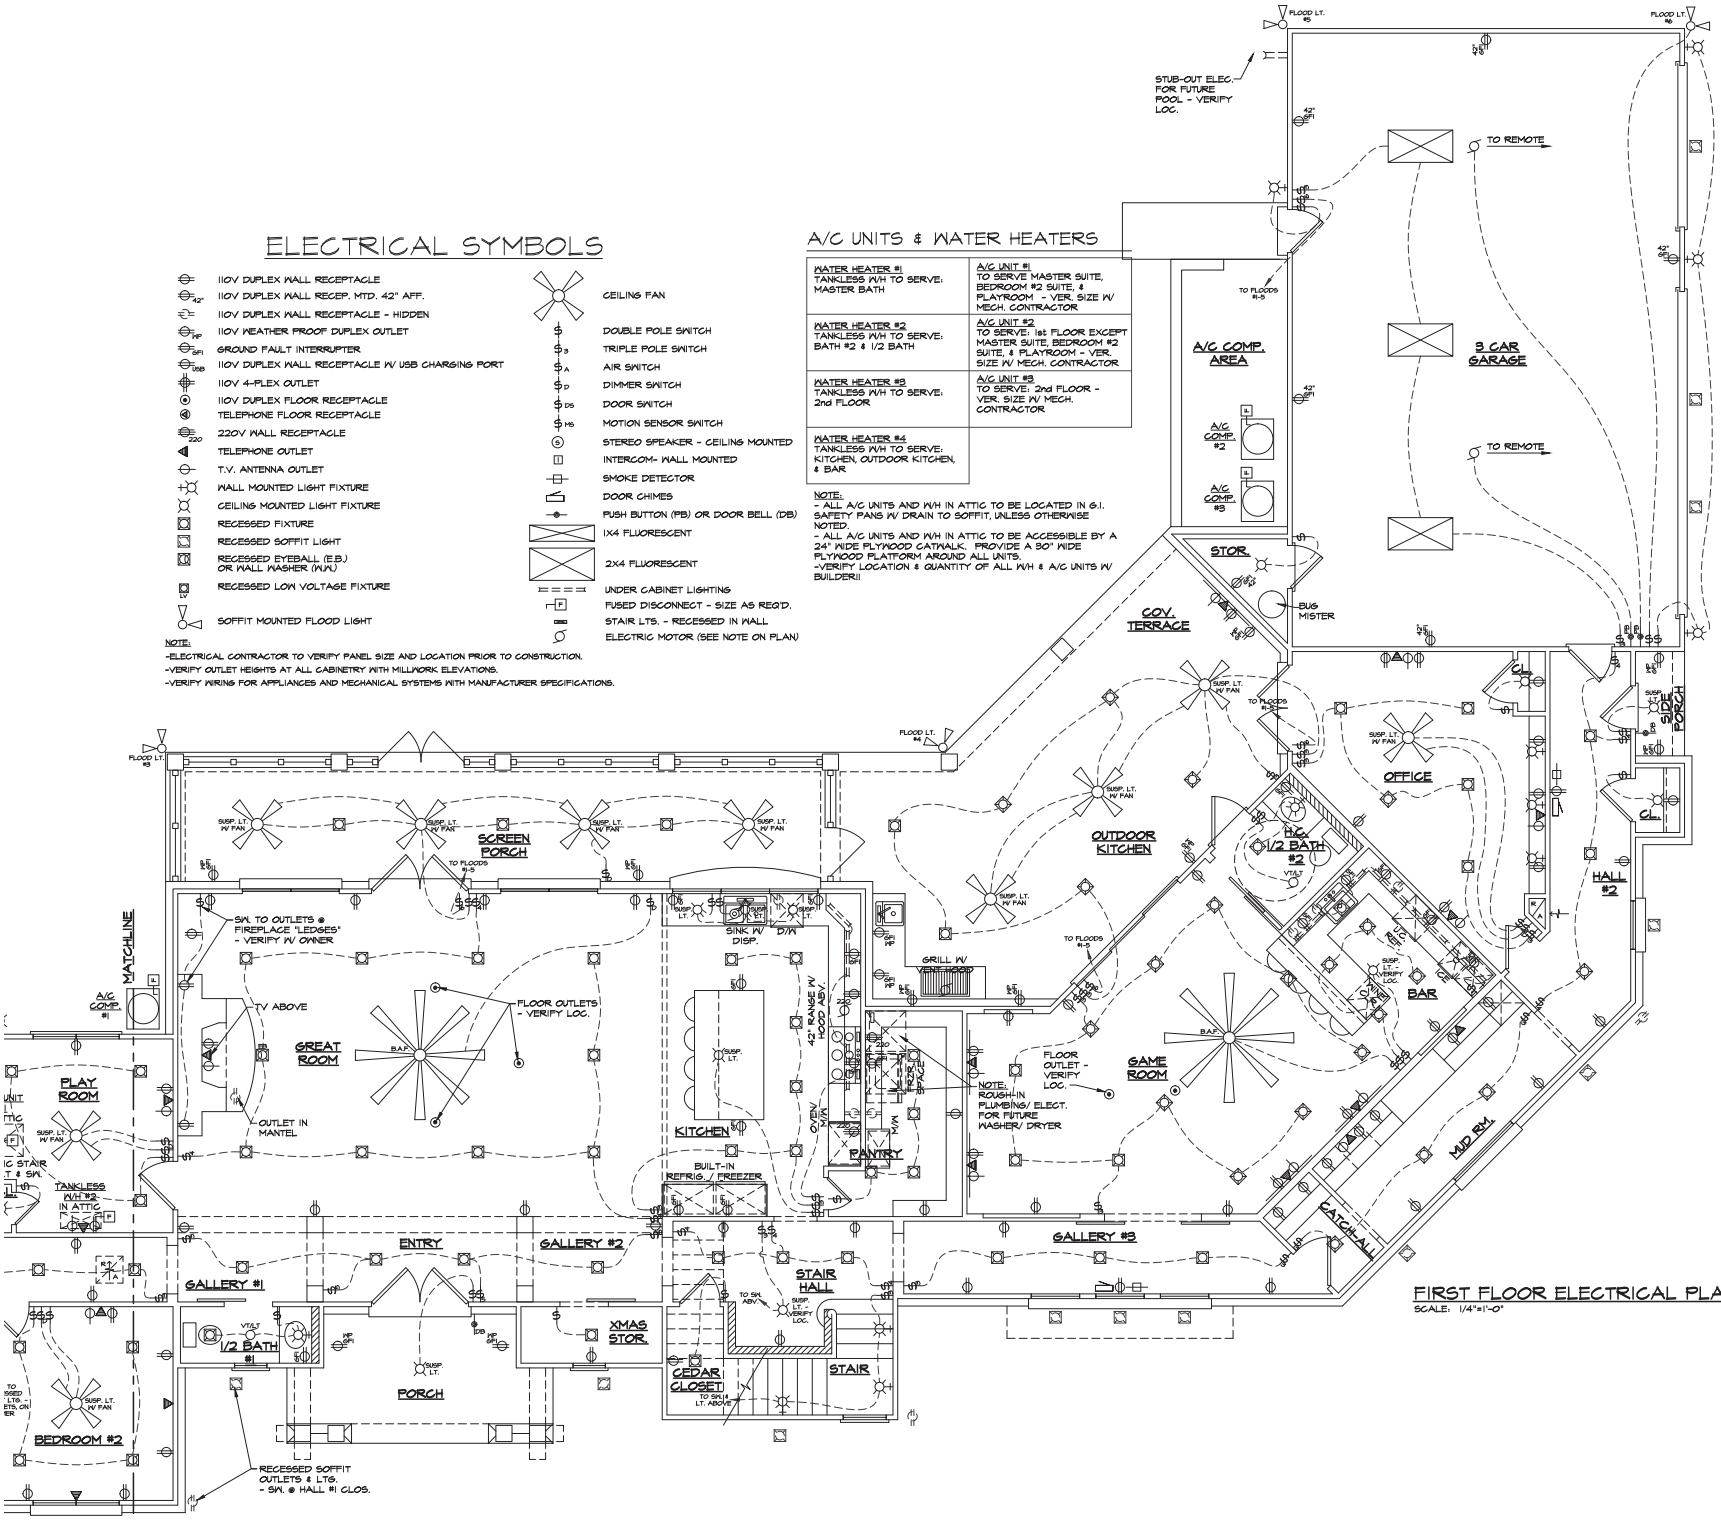

FIRST FLOOR ELECTRICAL PLAN - PART "A"
SCALE: 1/4"=1'-0"